


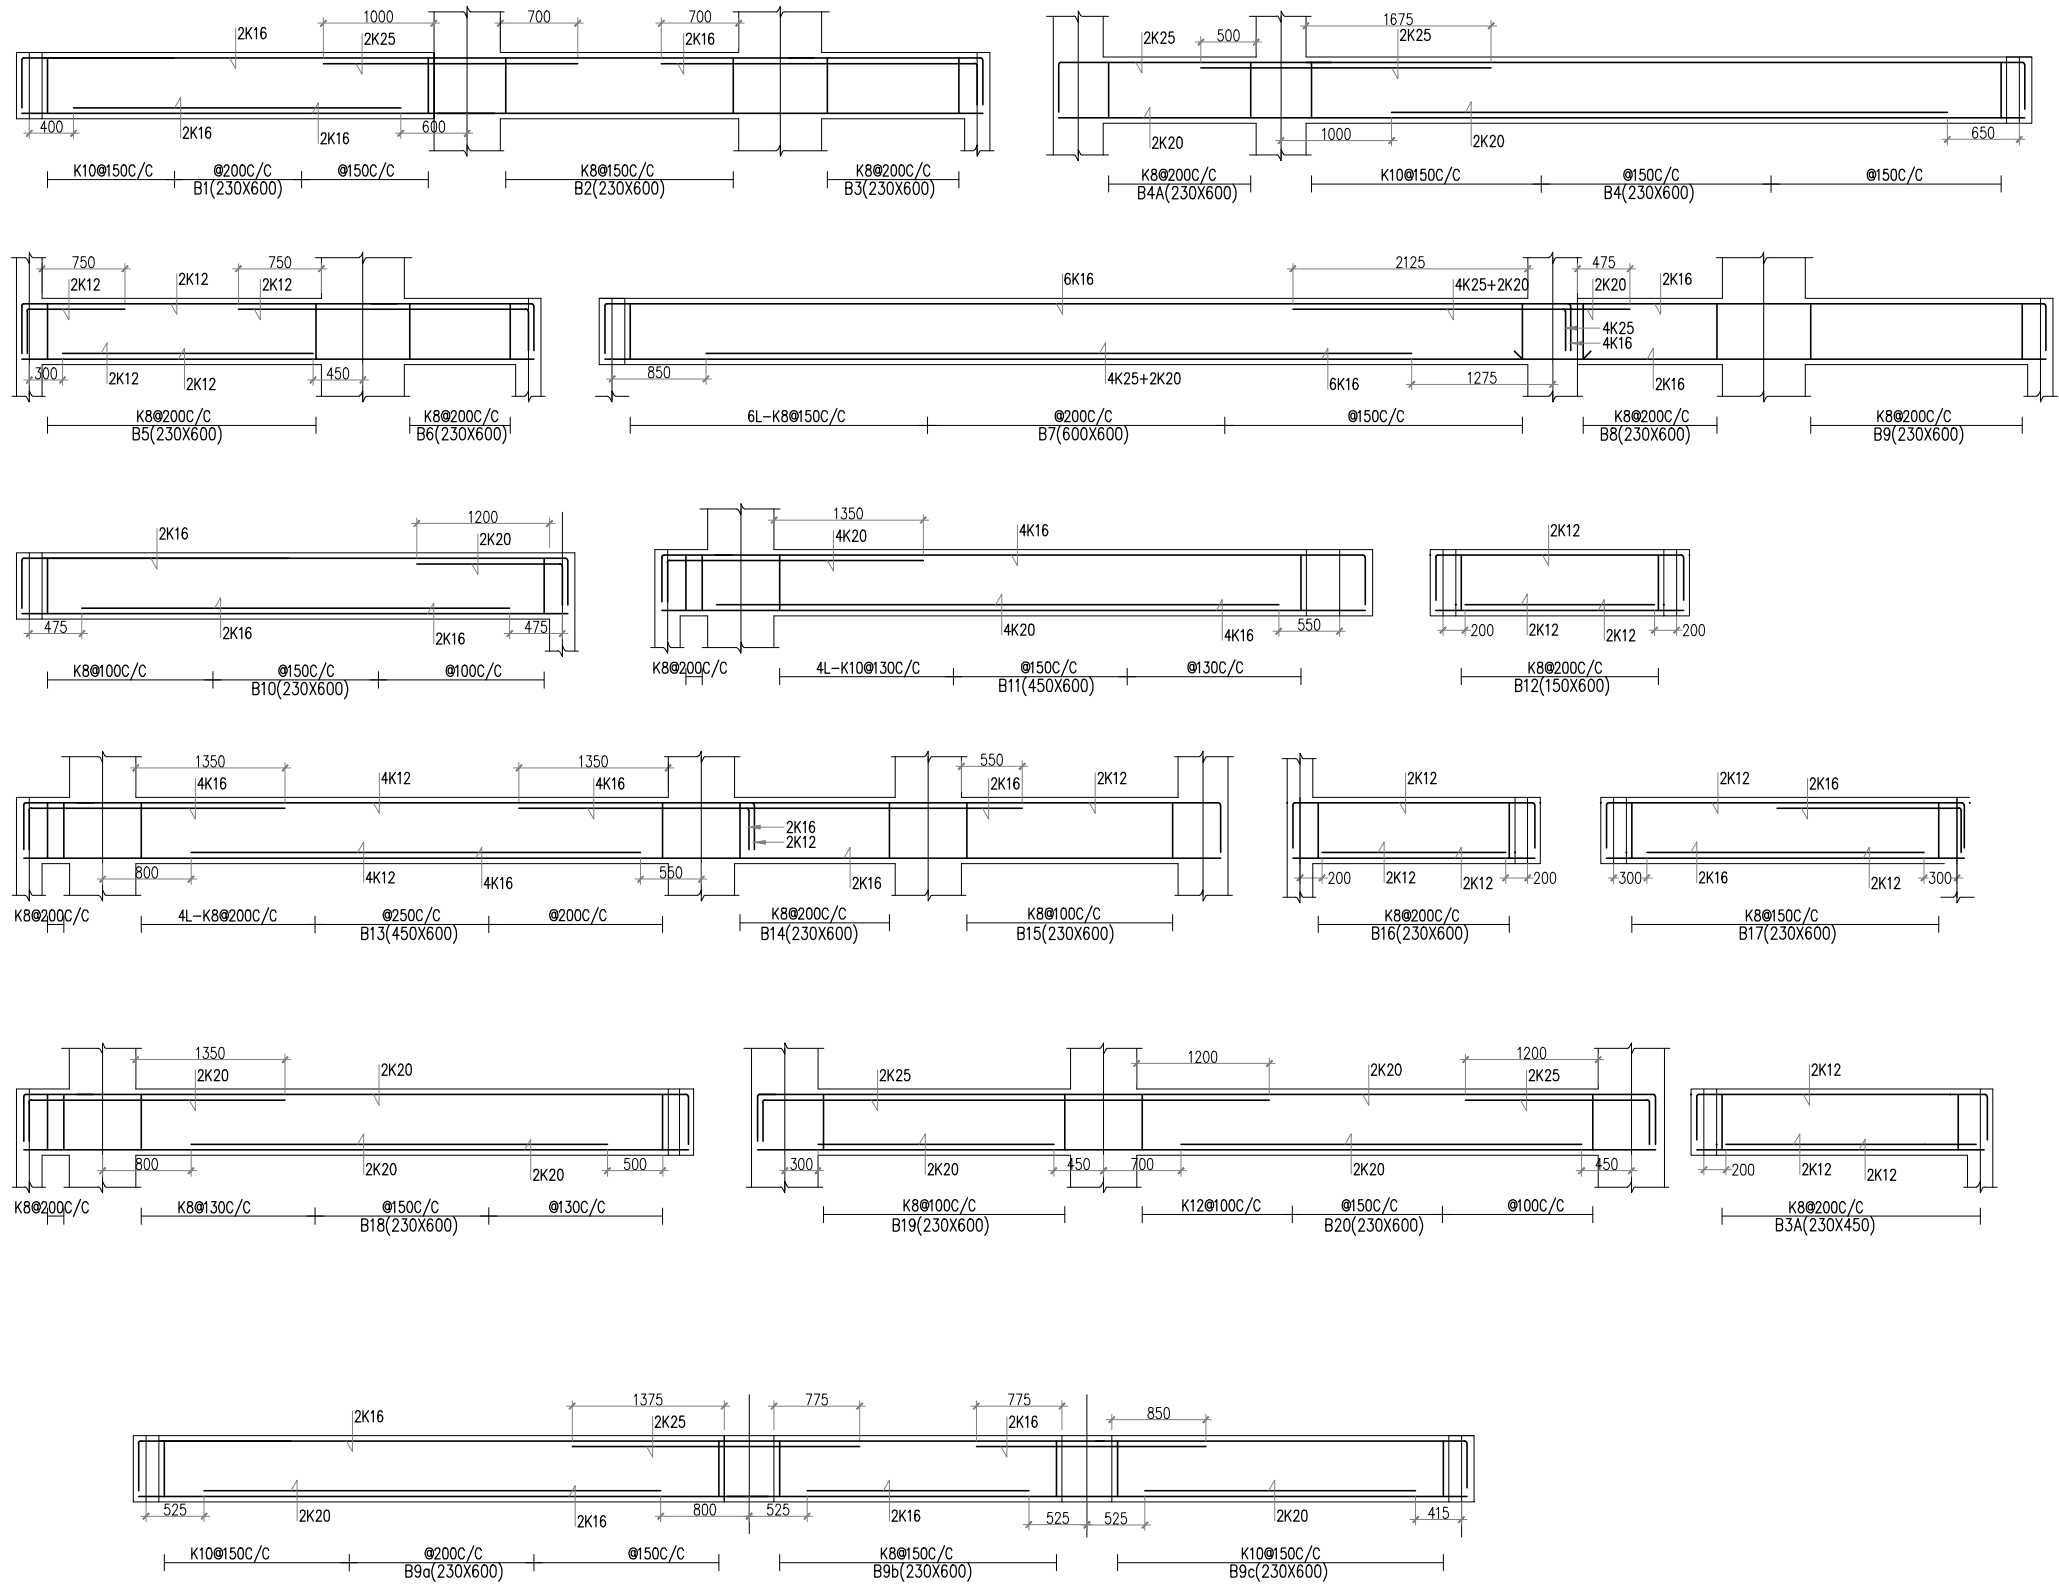

- NOTES:-
01. DRAWING SHALL BE READ, NOT MEASURED.
 02. GRADE OF STEEL Fe550.
 03. 'K' DENOTES TOR STEEL.
 04. ALL DIMENSIONS ARE IN MM.
 05. ALL LEVELS TO BE AS PER ARCHITECTURAL DRAWING ONLY.
 06. REF THIS DRG ALONG WITH ARCH. DRG.
 07. ANY DISCREPANCIES NOTED IN THE DRAWING SHOULD BE THE NOTICE OF THE STRUCTURAL CONSULTANT.
 08. READ THIS DWG ALONG WITH ARCHITECTURAL & MEP DRAWINGS
 09. GRADE OF CONCRETE
FOR STAIR CASE-M25
FOR ALL COLUMNS-REFER COLUMN CHART
FOR ALL SHEAR WALLS-REFER COLUMN CHART GRADE
FOR ALL RCC RETAINING WALLS-M25
FOR COMBINED/RAFT FOOTING-M25
FOR ISOLATED FOOTING-M25
 10. CONCRETE COVER FOR MAIN REINFORCEMENT
FOR ALL COLUMNS-40
FOR ALL RCC WALLS-20
FOR RAFT FOOTING-75
FOR ISOLATED FOOTING-50
 11. CURING OF CONCRETE SHALL BE FOR 21DAYS WITH POTABLE WATER
 12. STRUCTURAL CONSULTANTS ARE NOT RESPONSIBLE FOR STRUCTURES IF THE STRENGTH OF CONCRETE IS NOT ACHIEVED AT SITE BY CONTRACTOR AS SPECIFIED IN THE DRAWING.
 13. SBC CONSIDERED FOR FOUNDATION DESIGN IS 18 T/SQM
ADD REFER FOR SCHEDULE WHEREVER APPLICABLE.

△				
△				
△				
30.05.2028	GOOD FOR CONSTRUCTION		RAGHU	SANJAY
REVNO.	DATE	DESCRIPTION FOR REVISION	DRAWN BY/CHECKED BY	
PURPOSE:		PURPOSE:		
SEAL AND SIGNATURE OF STRUCTURAL ENGINEER		SEAL AND SIGNATURE OF ARCHITECT		
CLIENT:- N.J BUILDERS				
PROJECT:- NJ HORIZON				
TITLE GROUND FLOOR BEAM REINF, DETAILS				
DEALT/COORDINATED SANJAY	DESIGNED SANJAY		ORIENTATION	
DATE 30.05.2026	CONSULTANT DRAWING NO	JC-SD-115-02-02		
SCALE 1:50	STRUCTURAL DRAWING	ORIGINAL SHEET SIZE-A2	REVISION	
STRUCTURAL CONSULTANT	JAYCONSULTANTS CONSULTANTS & ENGINEERS		R0	CONSULTANT NO. 115