


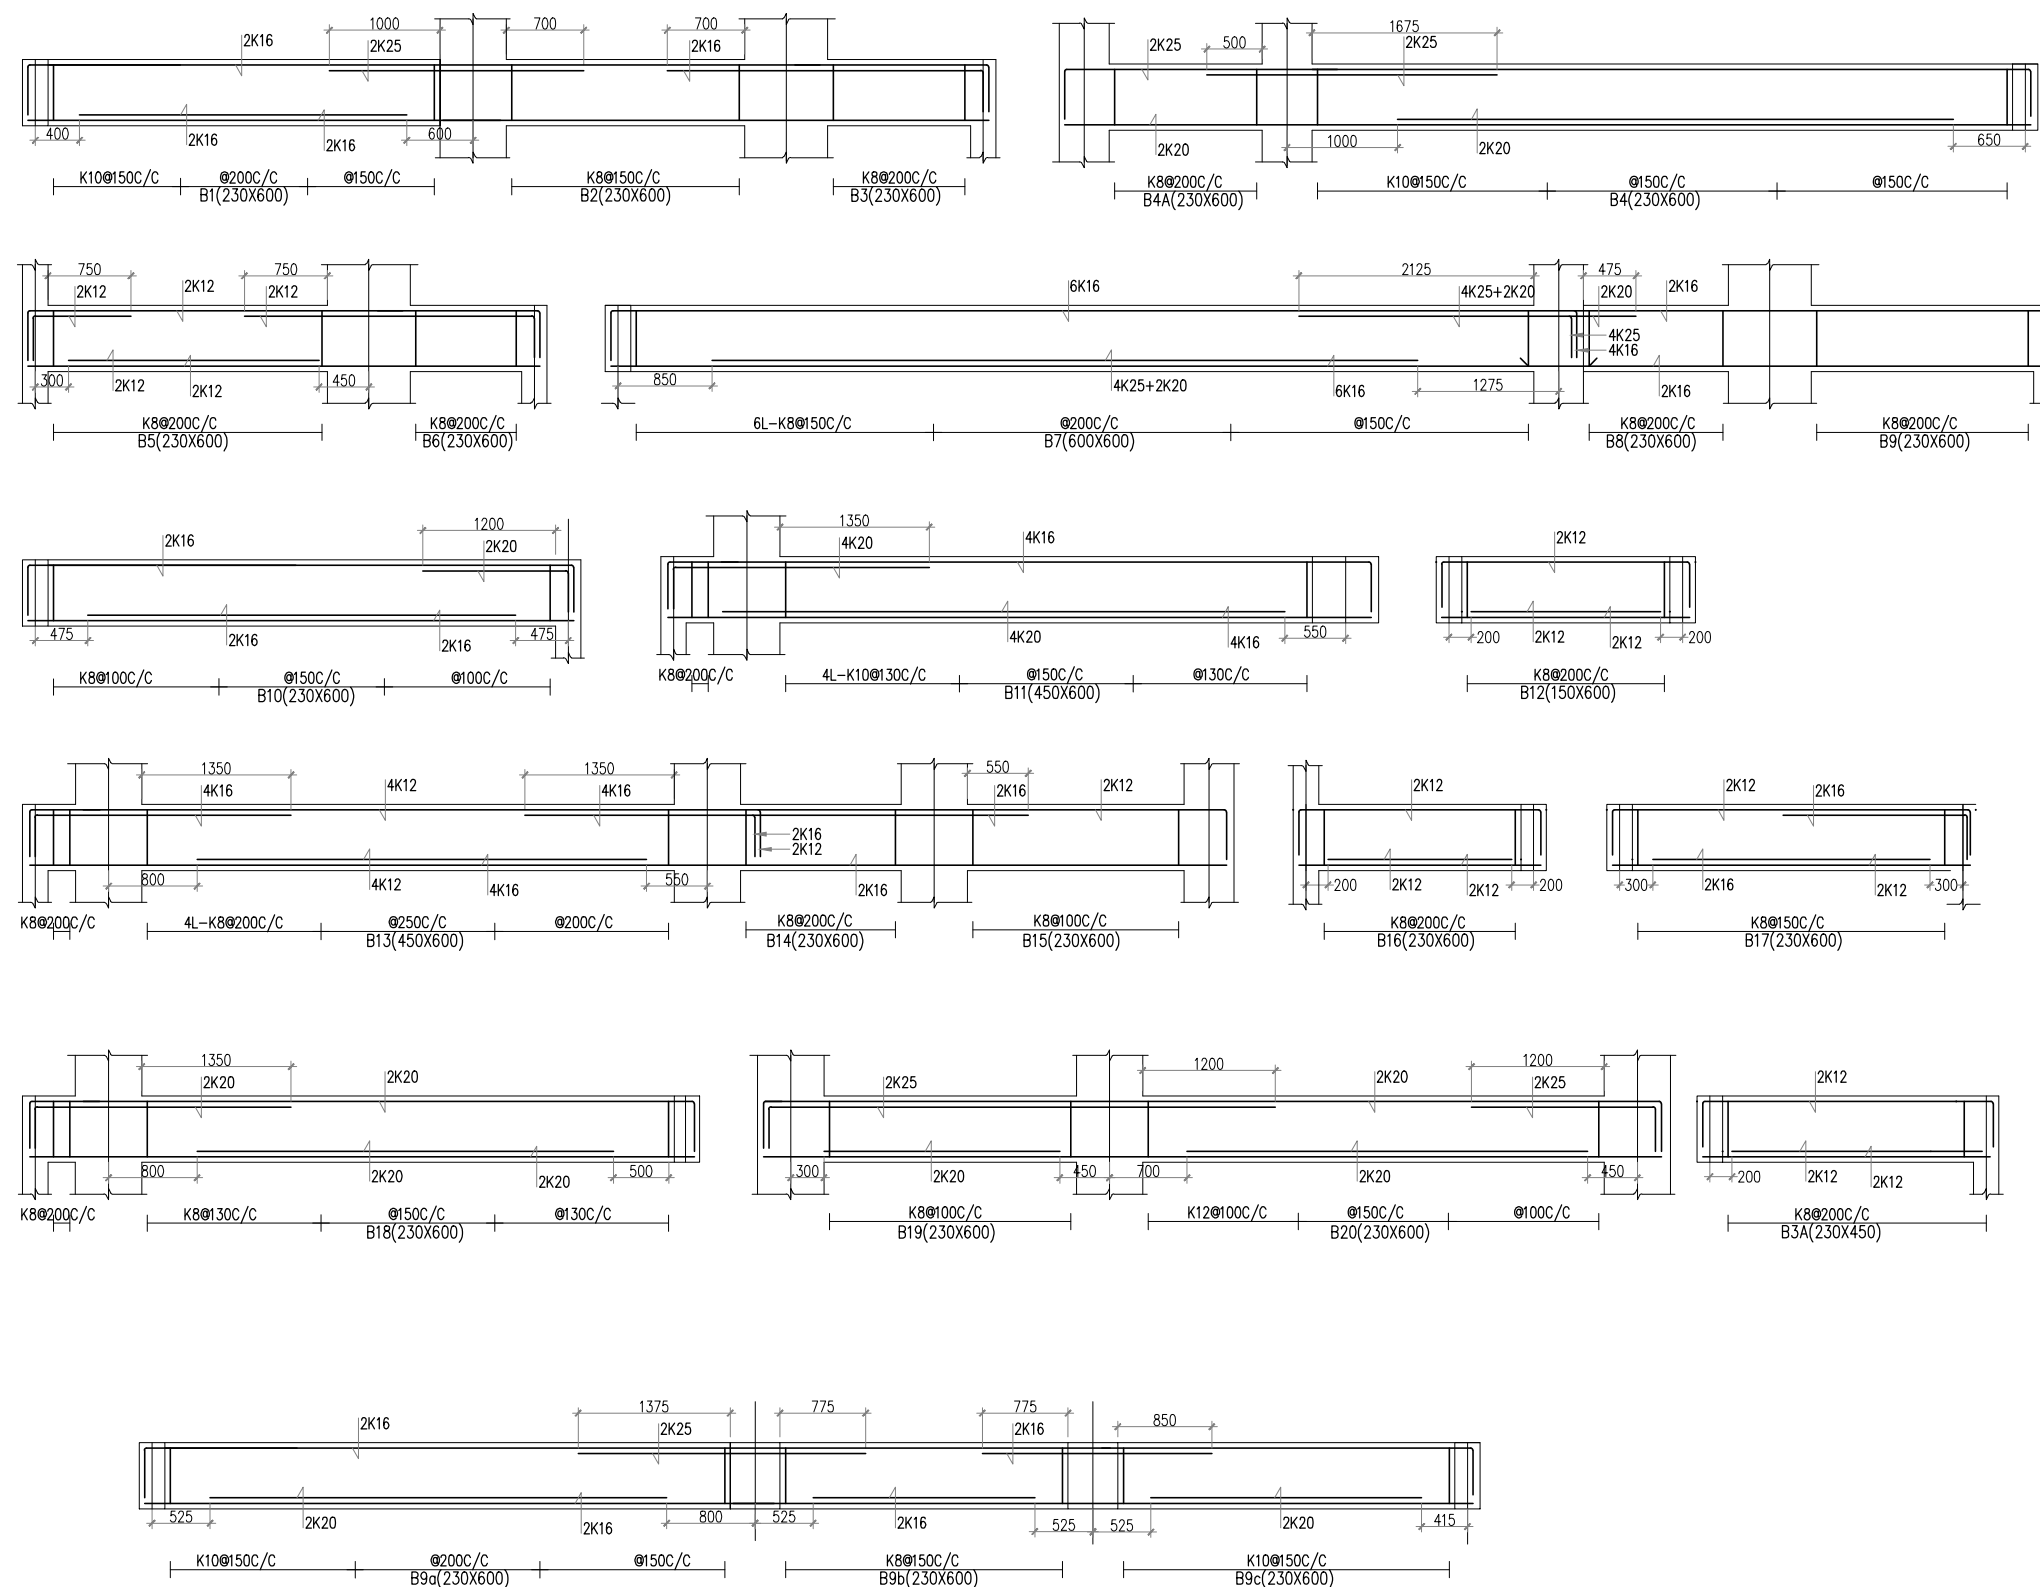

- NOTES:-**
01. DRAWING SHALL BE READ, NOT MEASURED.
 02. GRADE OF STEEL Fe550.
 03. 'K' DENOTES TOR STEEL.
 04. ALL DIMENSIONS ARE IN MM.
 05. ALL LEVELS TO BE AS PER ARCHITECTURAL DRAWING ONLY.
 06. REF THIS DRG ALONG WITH ARCH. DRG.
 07. ANY DISCREPANCIES NOTED IN THE DRAWING SHOULD BE THE NOTICE OF THE STRUCTURAL CONSULTANT.
 08. READ THIS DWG ALONG WITH ARCHITECTURAL & MEP DRAWINGS
 09. GRADE OF CONCRETE
 - FOR STAIR CASE-M25
 - FOR ALL COLUMNS-REFER COLUMN CHART
 - FOR ALL SHEAR WALLS-REFER COLUMN CHART GRADE
 - FOR ALL RCC RETAINING WALLS-M25
 - FOR COMBINED/RAFT FOOTING-M25
 - FOR ISOLATED FOOTING-M25
 10. CONCRETE COVER FOR MAIN REINFORCEMENT
 - FOR ALL COLUMNS-40
 - FOR ALL RCC WALLS-20
 - FOR RAFT FOOTING-75
 - FOR ISOLATED FOOTING-50
 11. CURING OF CONCRETE SHALL BE FOR 21DAYS WITH POTABLE WATER
 12. STRUCTURAL CONSULTANTS ARE NOT RESPONSIBLE
 - FOR STRUCTURES IF THE STRENGTH OF CONCRETE IS NOT ACHIEVED AT SITE BY CONTRACTOR AS SPECIFIED IN THE DRAWING.
 13. SBC CONSIDERED FOR FOUNDATION DESIGN IS 18 T/SOM
ADD REFER FOR SCHEDULE WHEREVER APPLICABLE.

△					
△					
△					
NO.	30.05.2026	GOOD FOR CONSTRUCTION		RAGHU	SANJAY
REVNO.	DATE	DESCRIPTION FOR REVISION		DRAWN BY (CHECKED BY)	
PURPOSE:			PURPOSE:		
SEAL AND SIGNATURE OF STRUCTURAL ENGINEER			SEAL AND SIGNATURE OF ARCHITECT		
CLIENT:- N J BUILDERS					
PROJECT:- NJ HORIZON					
TITLE GROUND FLOOR BEAM REINF, DETAILS					
DEALT/COORDINATED SANJAY		DESIGNED SANJAY		ORIENTATION	
DATE 30.05.2026		CONSULTANT DRAWING NO JC-SD-115-02-02			
SCALE 1:50		STRUCTURAL DRAWING		REVISION	
STRUCTURAL CONSULTANT		ORIGINAL SHEET SIZE-A3		R0	
				CONS. JOB NO. 115	